


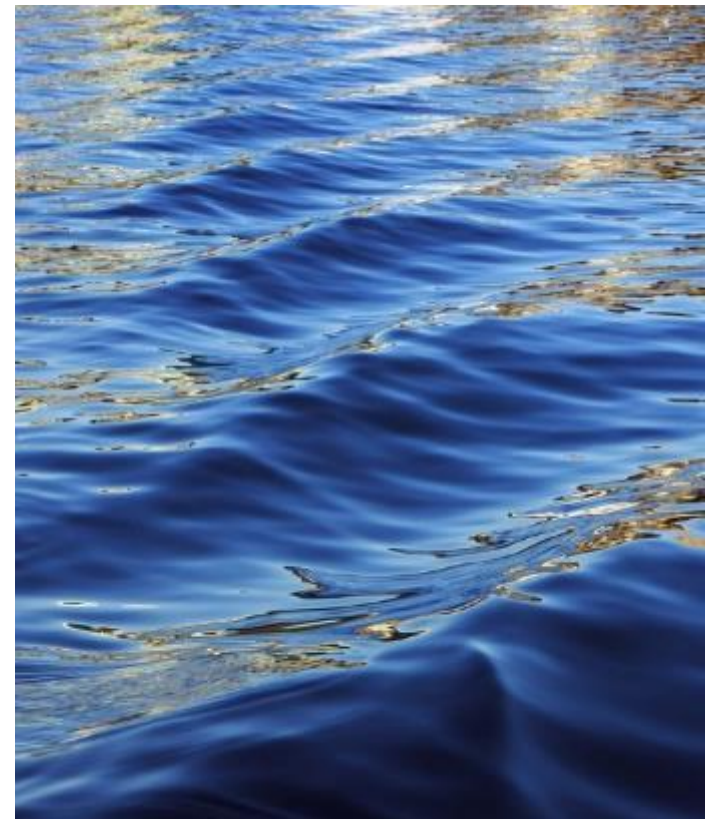

綠源科技股份有限公司

現場工程師養成計畫 (八)





第八堂課

施工圖面解析與現場檢核






現場監工必修10堂課

項次	課程
一	監工五大核心技能與責任
二	工程進度掌控與甘特圖運用
三	工程合約與施工規範重點
四	太陽能系統工程施工解析
五	儲能系統工程施工解析
六	電力系統與配電材料介紹
七	勞工安全衛生與每日表單
八	施工圖面解析與現場檢核
九	工程現場缺失案例與改善
十	案場施工查驗項目與表單




一、施工圖面解析

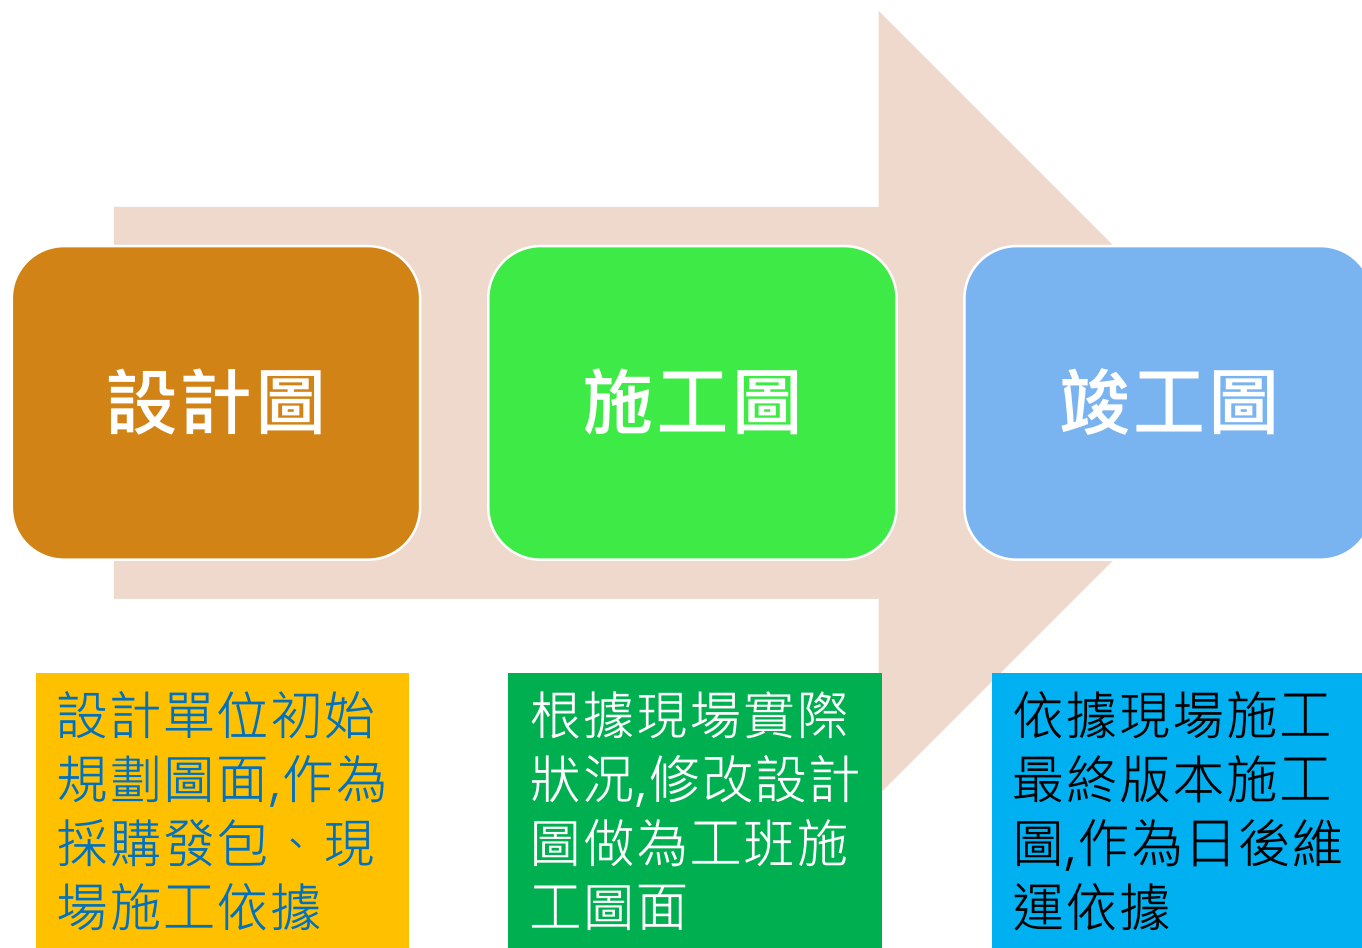

工程圖流程


圖面類別	說明
單線圖	電力系統架構說明
昇位圖	不同高度間設備管線連接說明
平面圖	設備平面排布說明
配置圖	管路/線槽平面配置說明
箱體圖	交直流箱體尺寸/器材配置說明

圖說類別

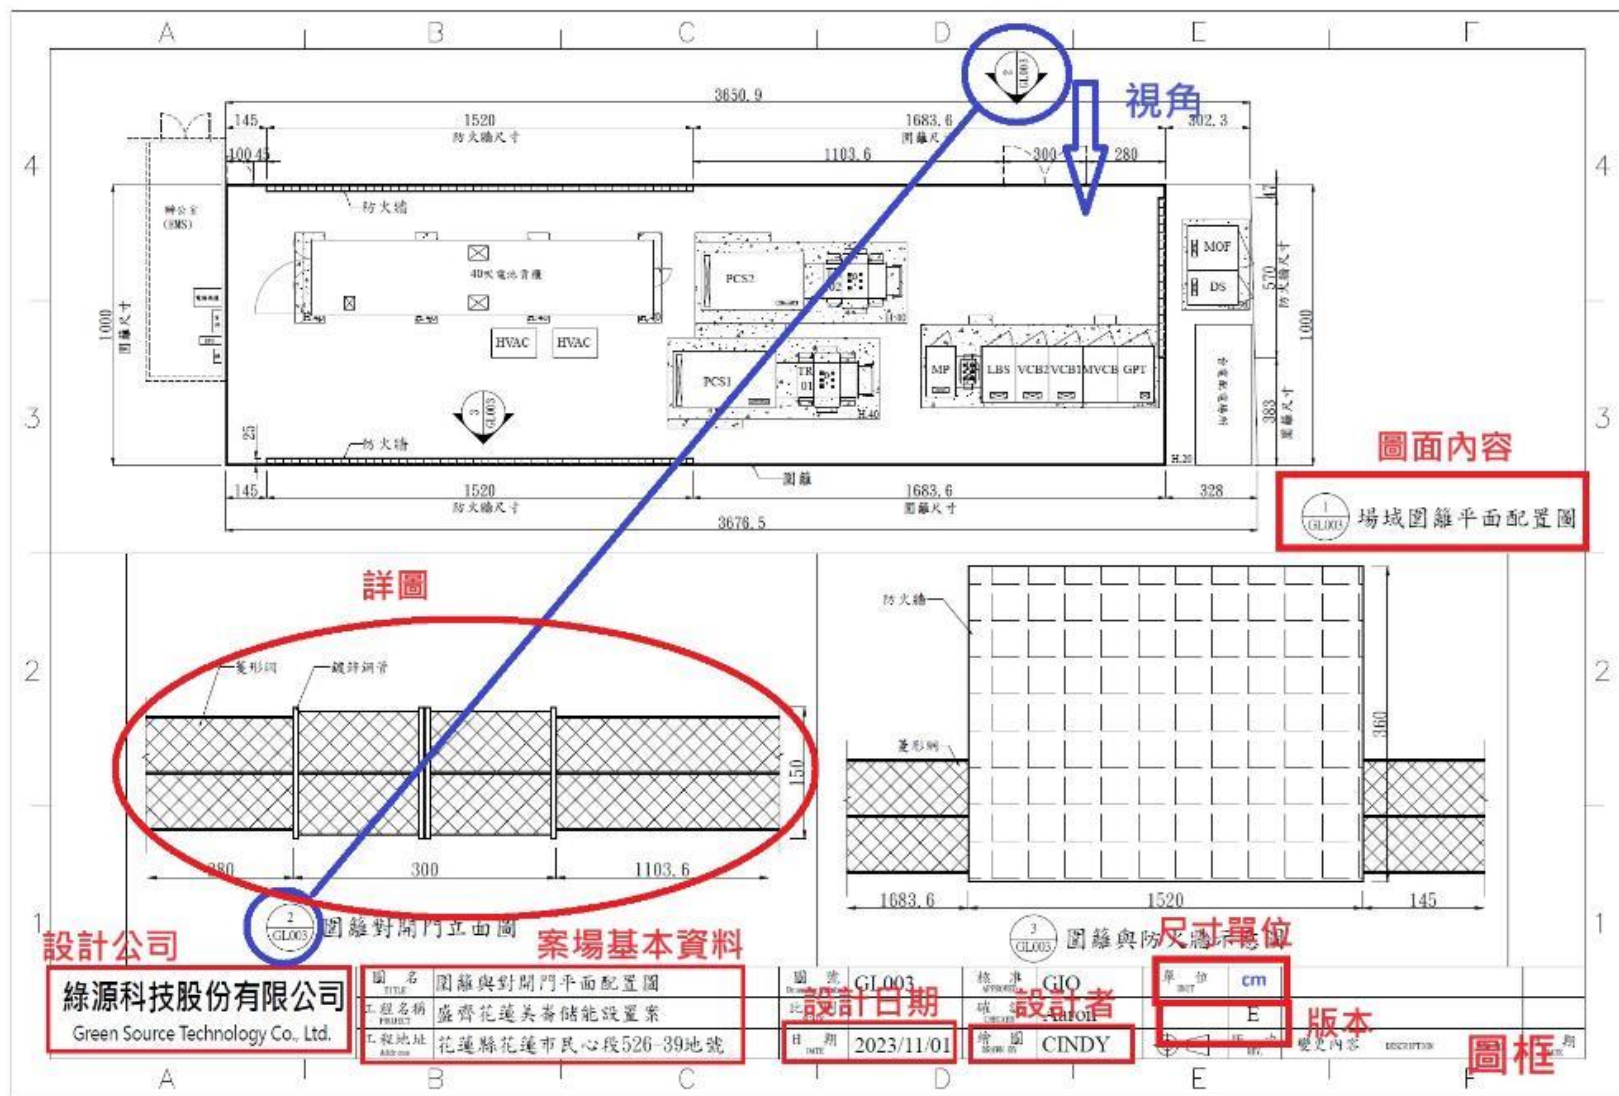

圖說結構

圖說結構

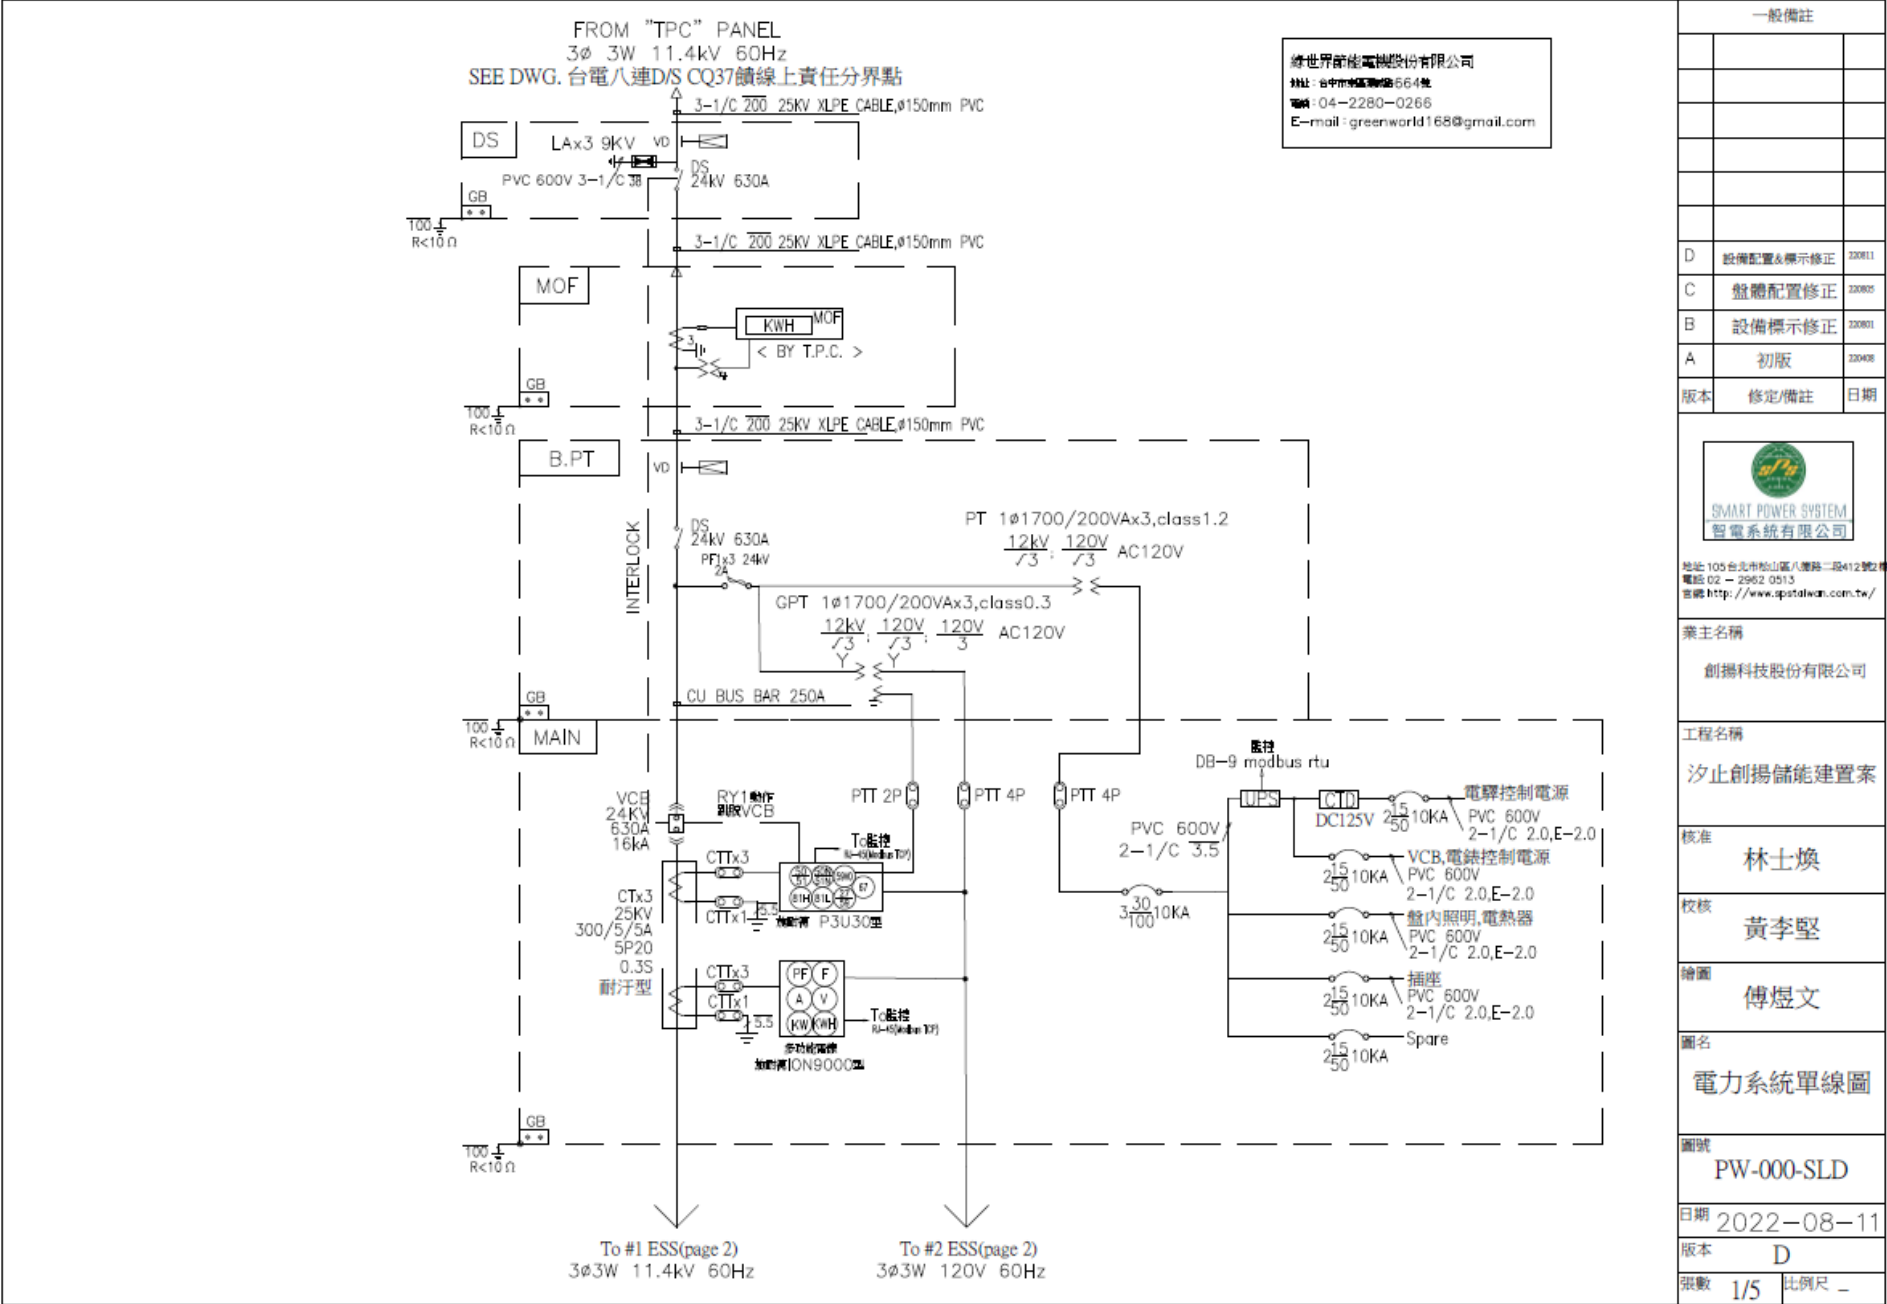


一般備註		
D	設備配置及標示修正	220811
C	盤體配置修正	220805
B	設備標示修正	220801
A	初版	220808
版本	修定/備註	日期
 地址: 105台北市松山區八德路二段412號2樓 電話: 02-2962 0513 官網: http://www.spatale.com.tw/ 業主名稱 創揚科技股份有限公司 工程名稱 汐止創揚儲能建置案 核准 林士煥 校核 黃李堅 繪圖 傅煜文 圖名 電力系統單線圖 圖號 PW-000-SLD 日期 2022-08-11 版本 D 張數 1/5 比例尺 -		


單線圖

FROM "TPC" PANEL
3 ϕ 3W 11.4kV 60Hz
SEE DWG. 台電八連D/S CQ37饋線上責任分界點


綠世界節能電機股份有限公司
地址：台中市西區西門路664號
電話：04-2280-0266
E-mail: greenworld168@gmail.com

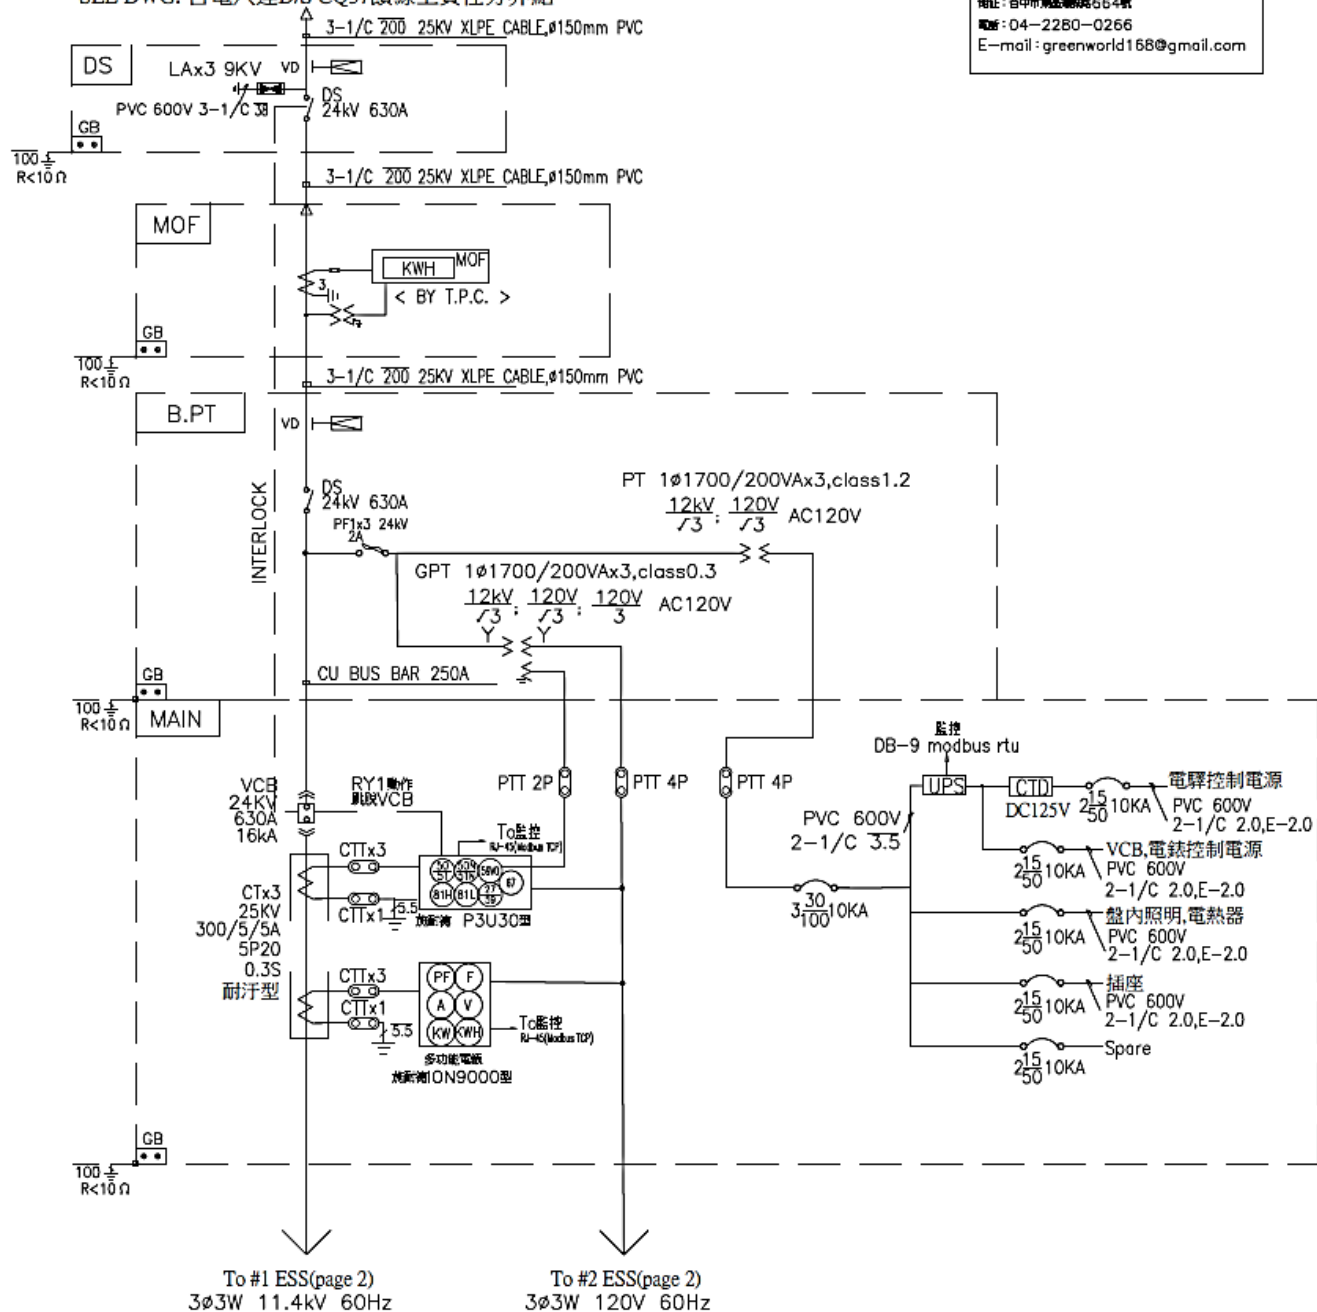


昇位圖

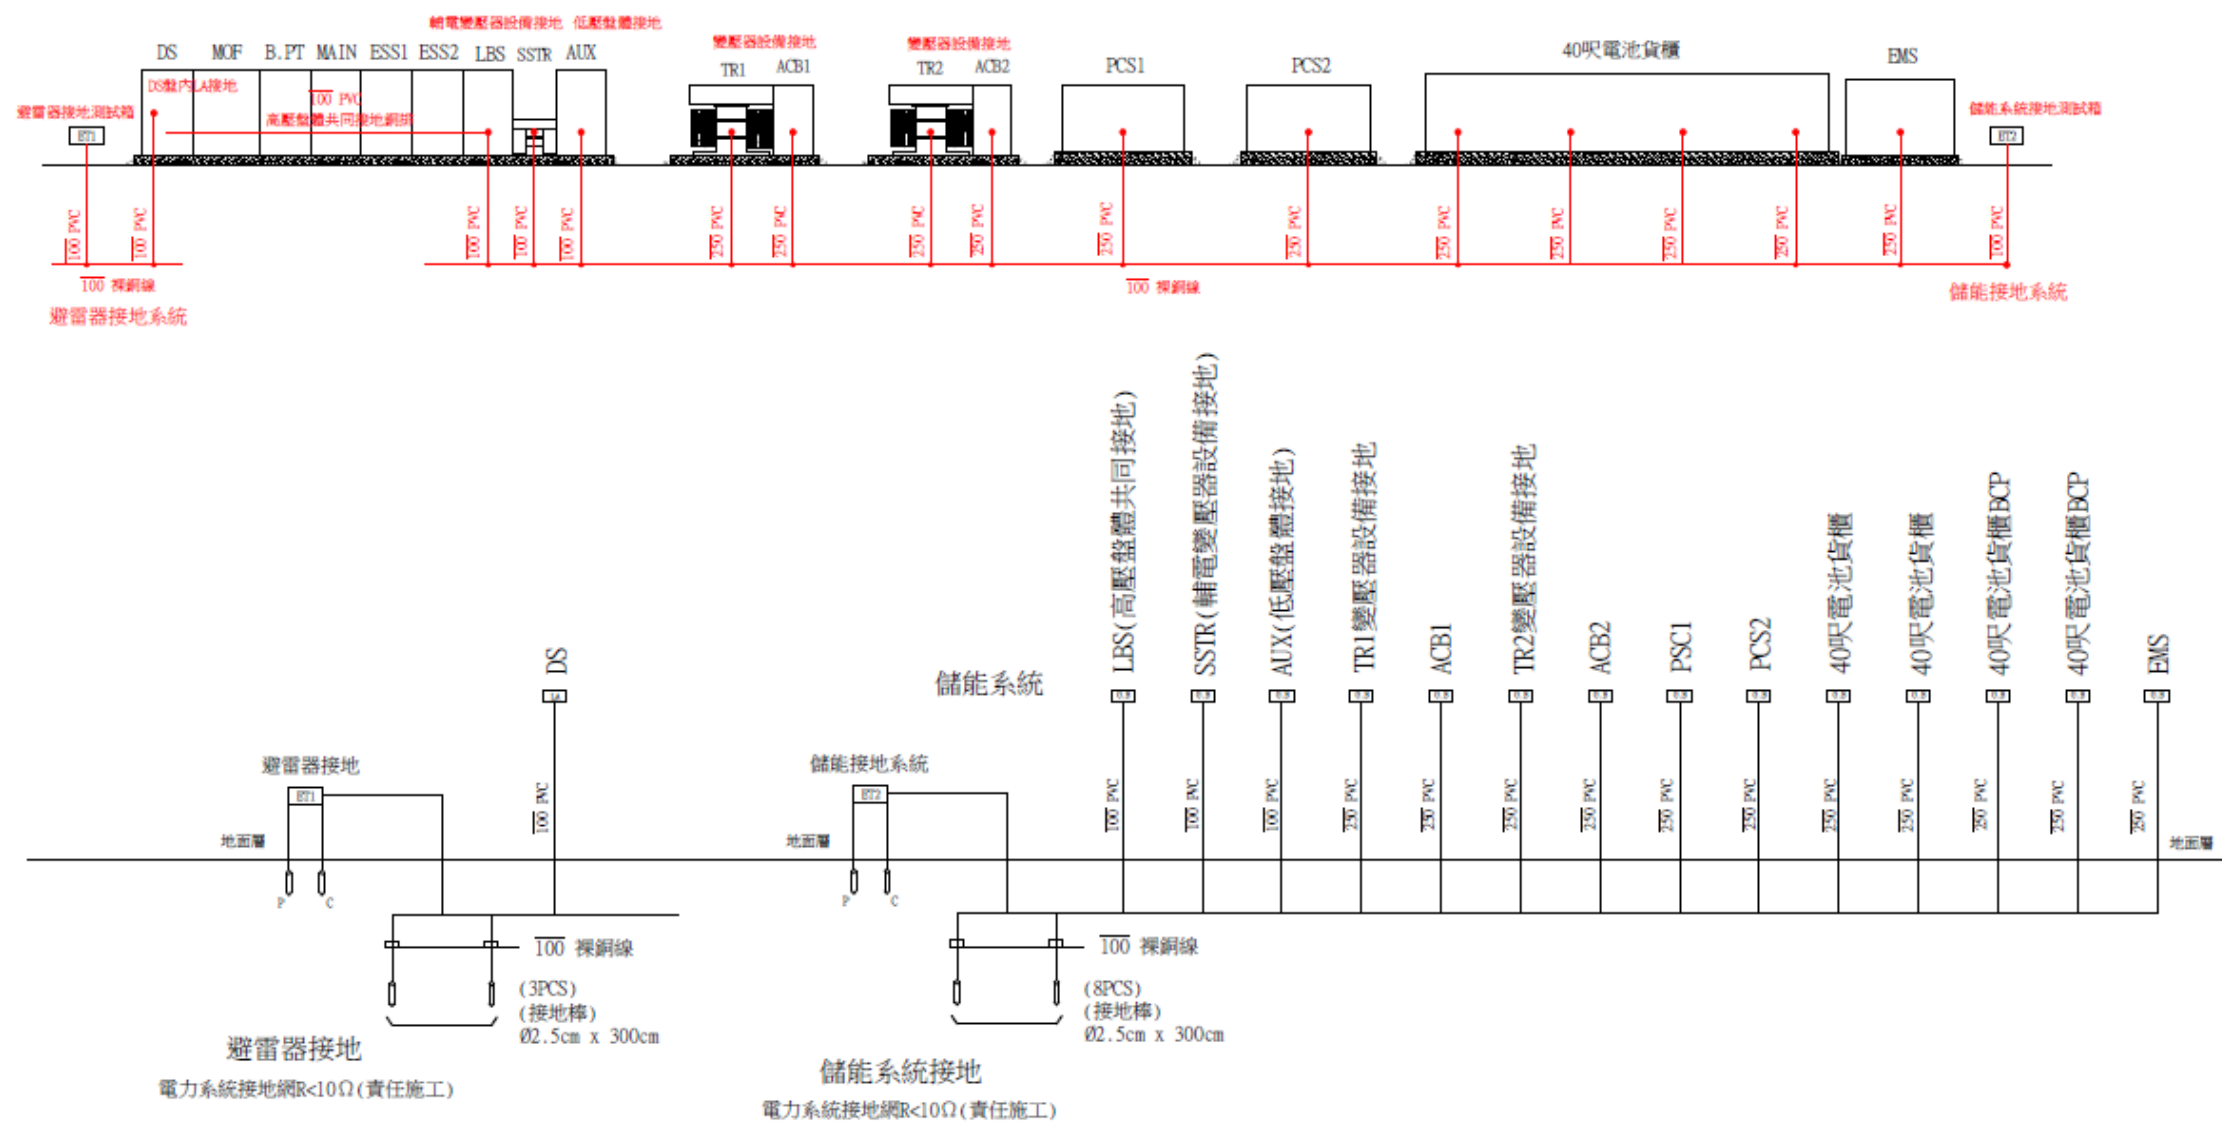

昇位圖

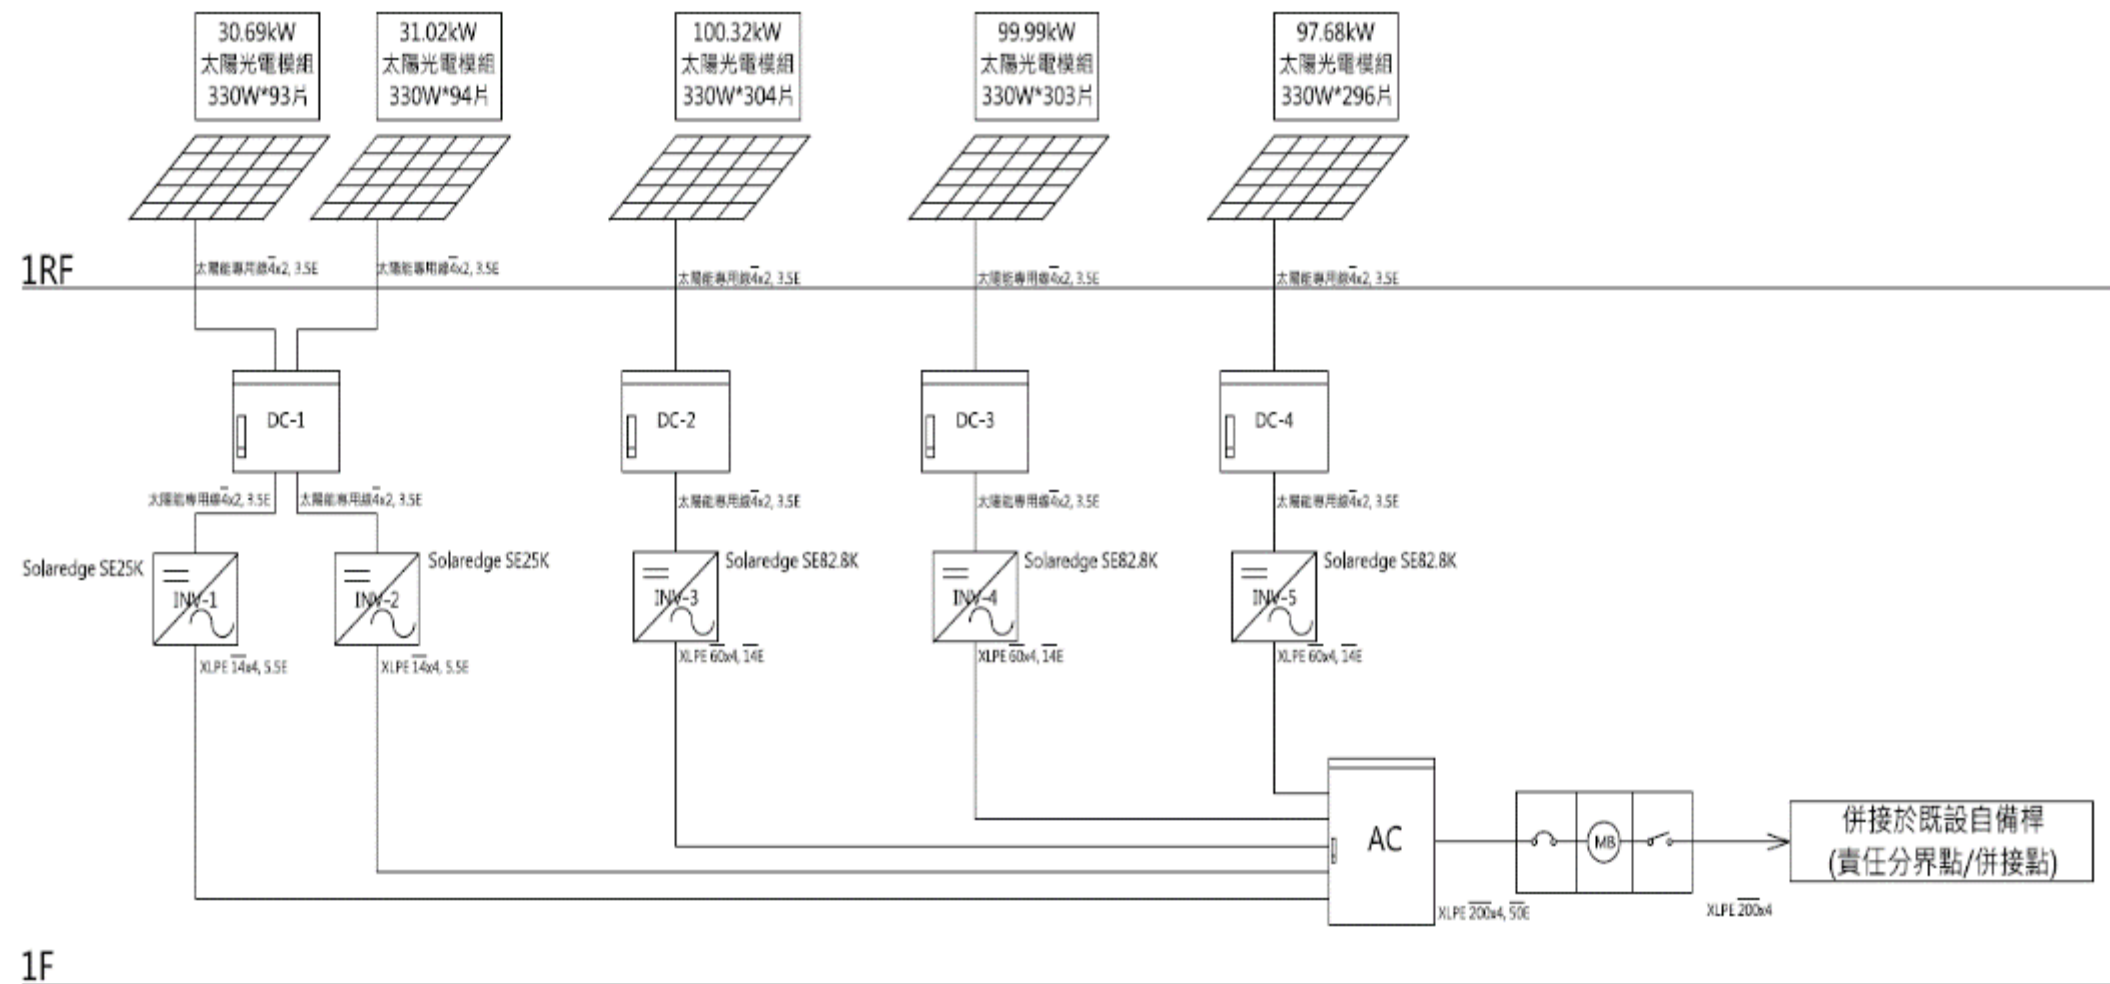


平面圖

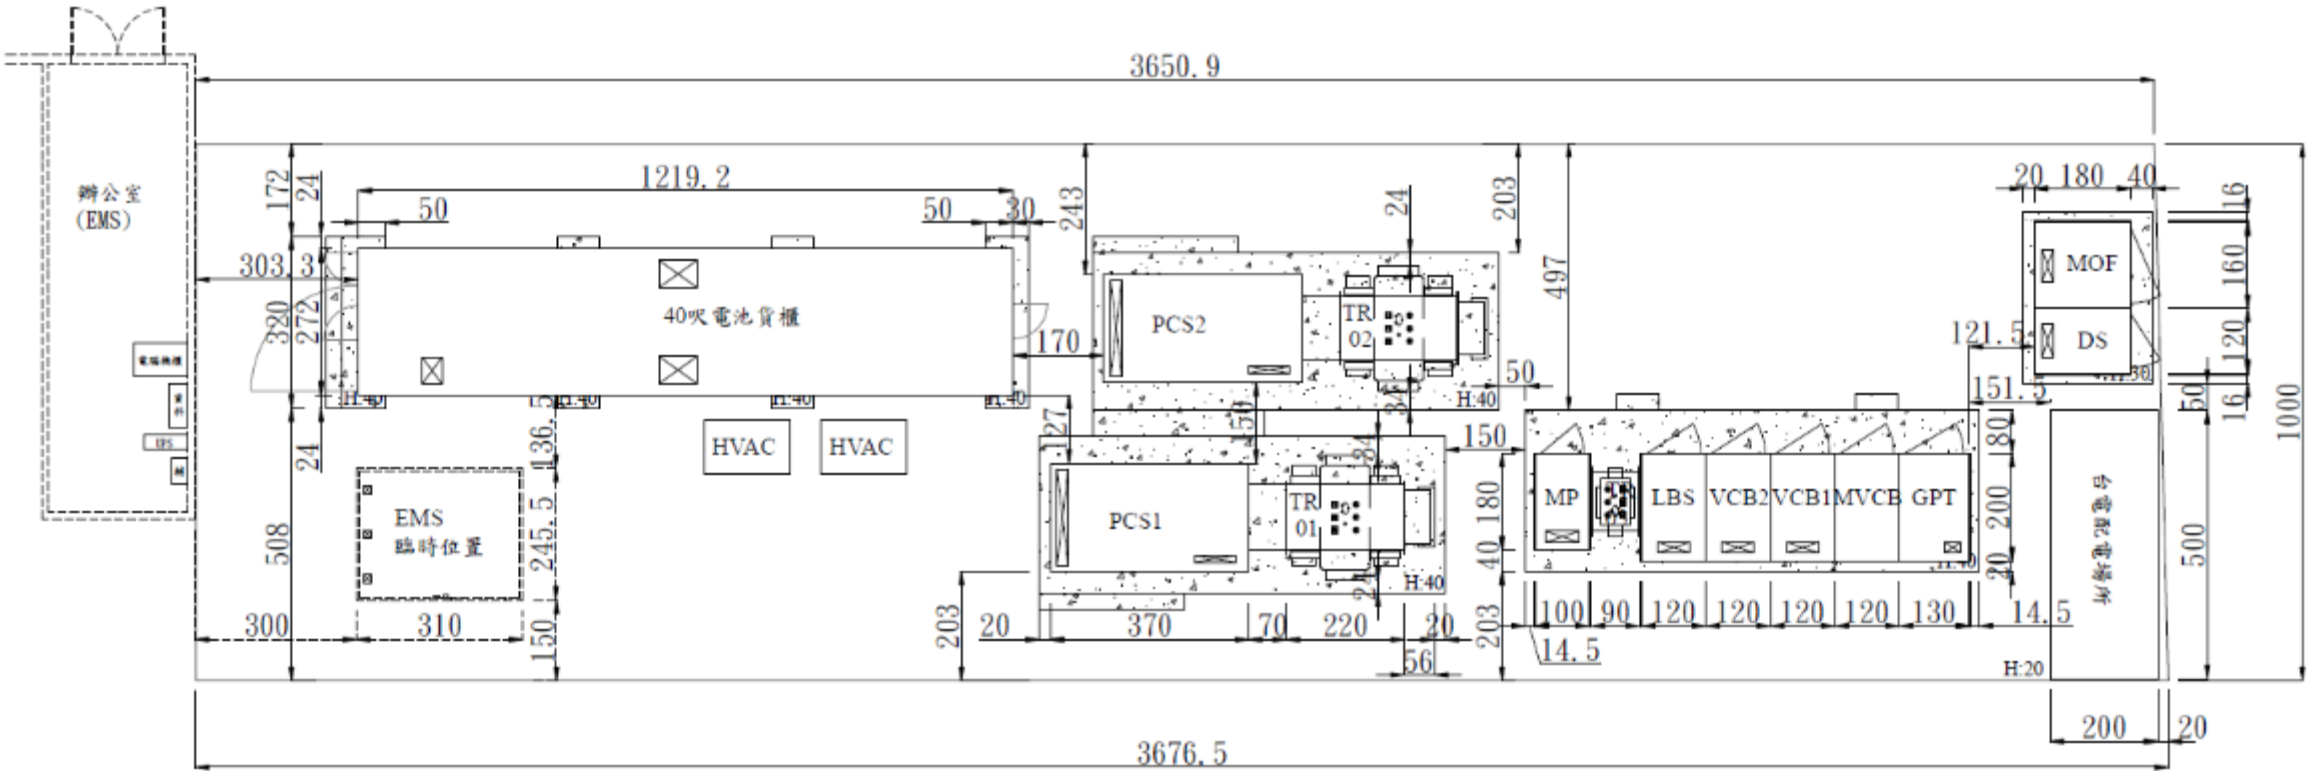

1
GL001 儲能設備平面配置圖


平面圖

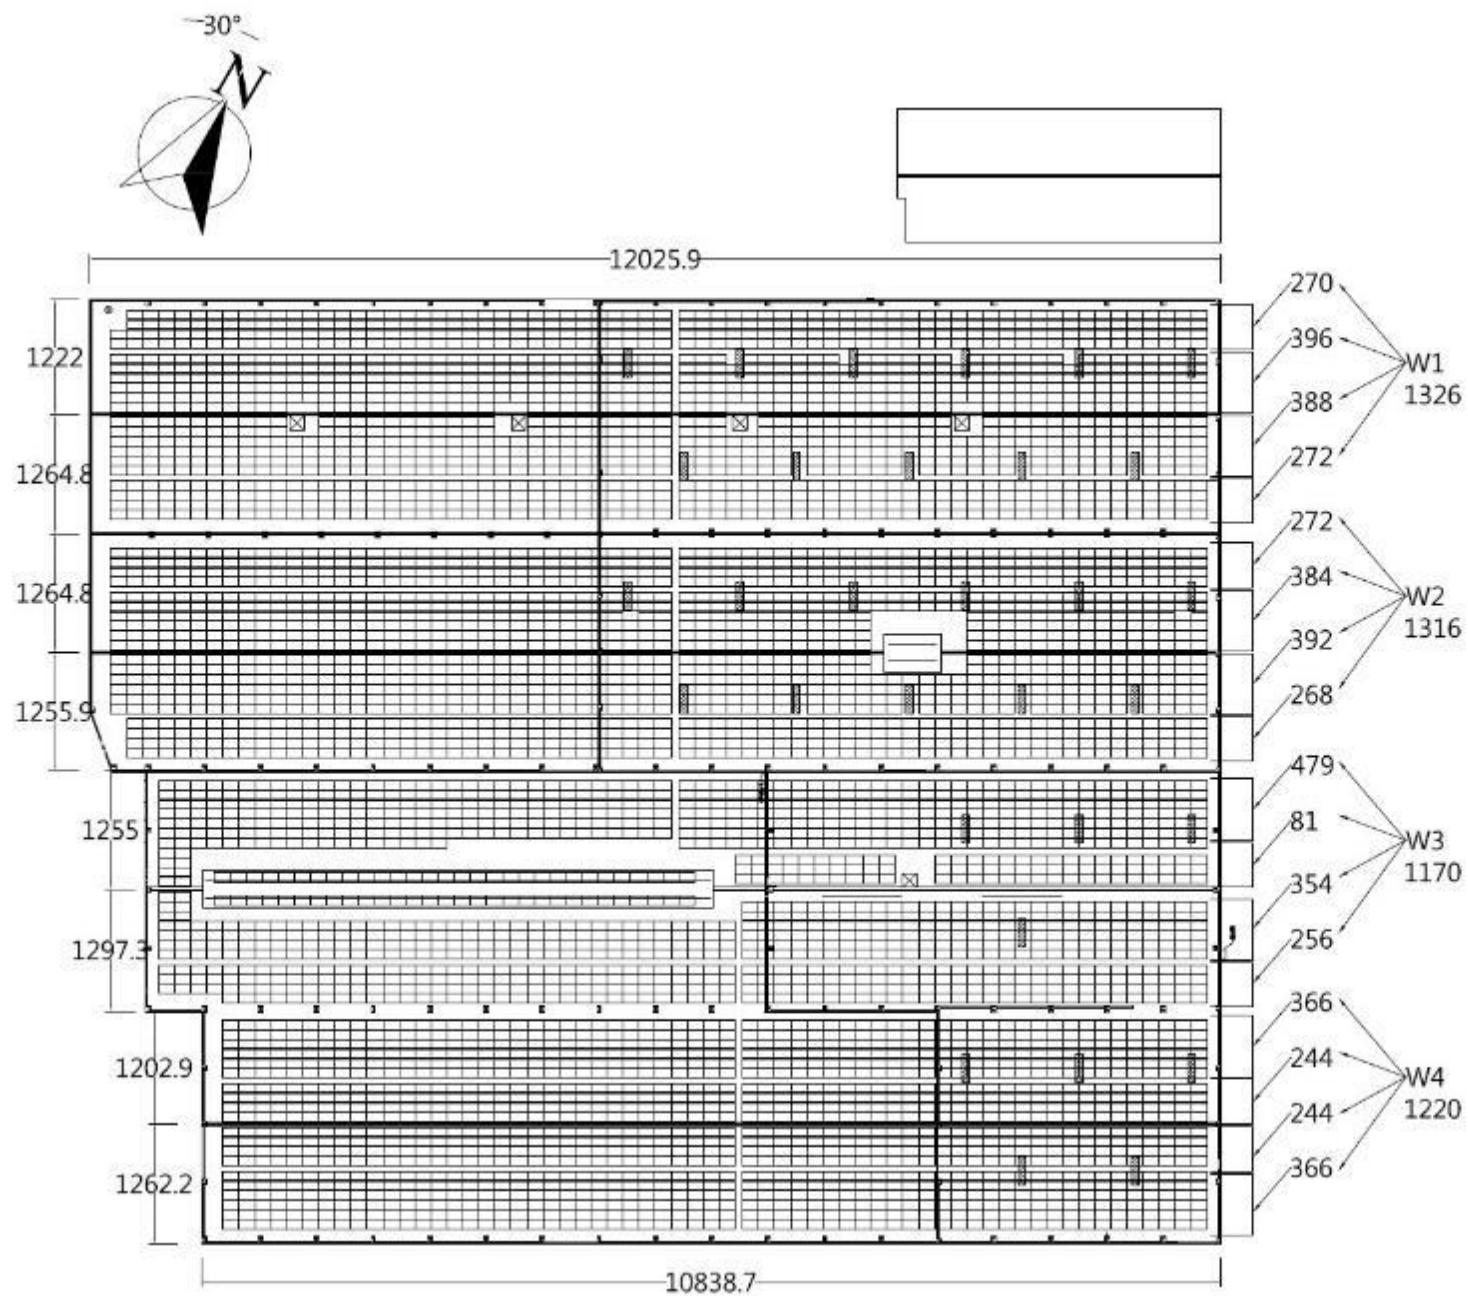

工廠屋頂模組片數:
 $1326 + 1316 + 1170 + 1220 = 5032$ 片


變流器型號: PV-75000T-U 20台

配置圖

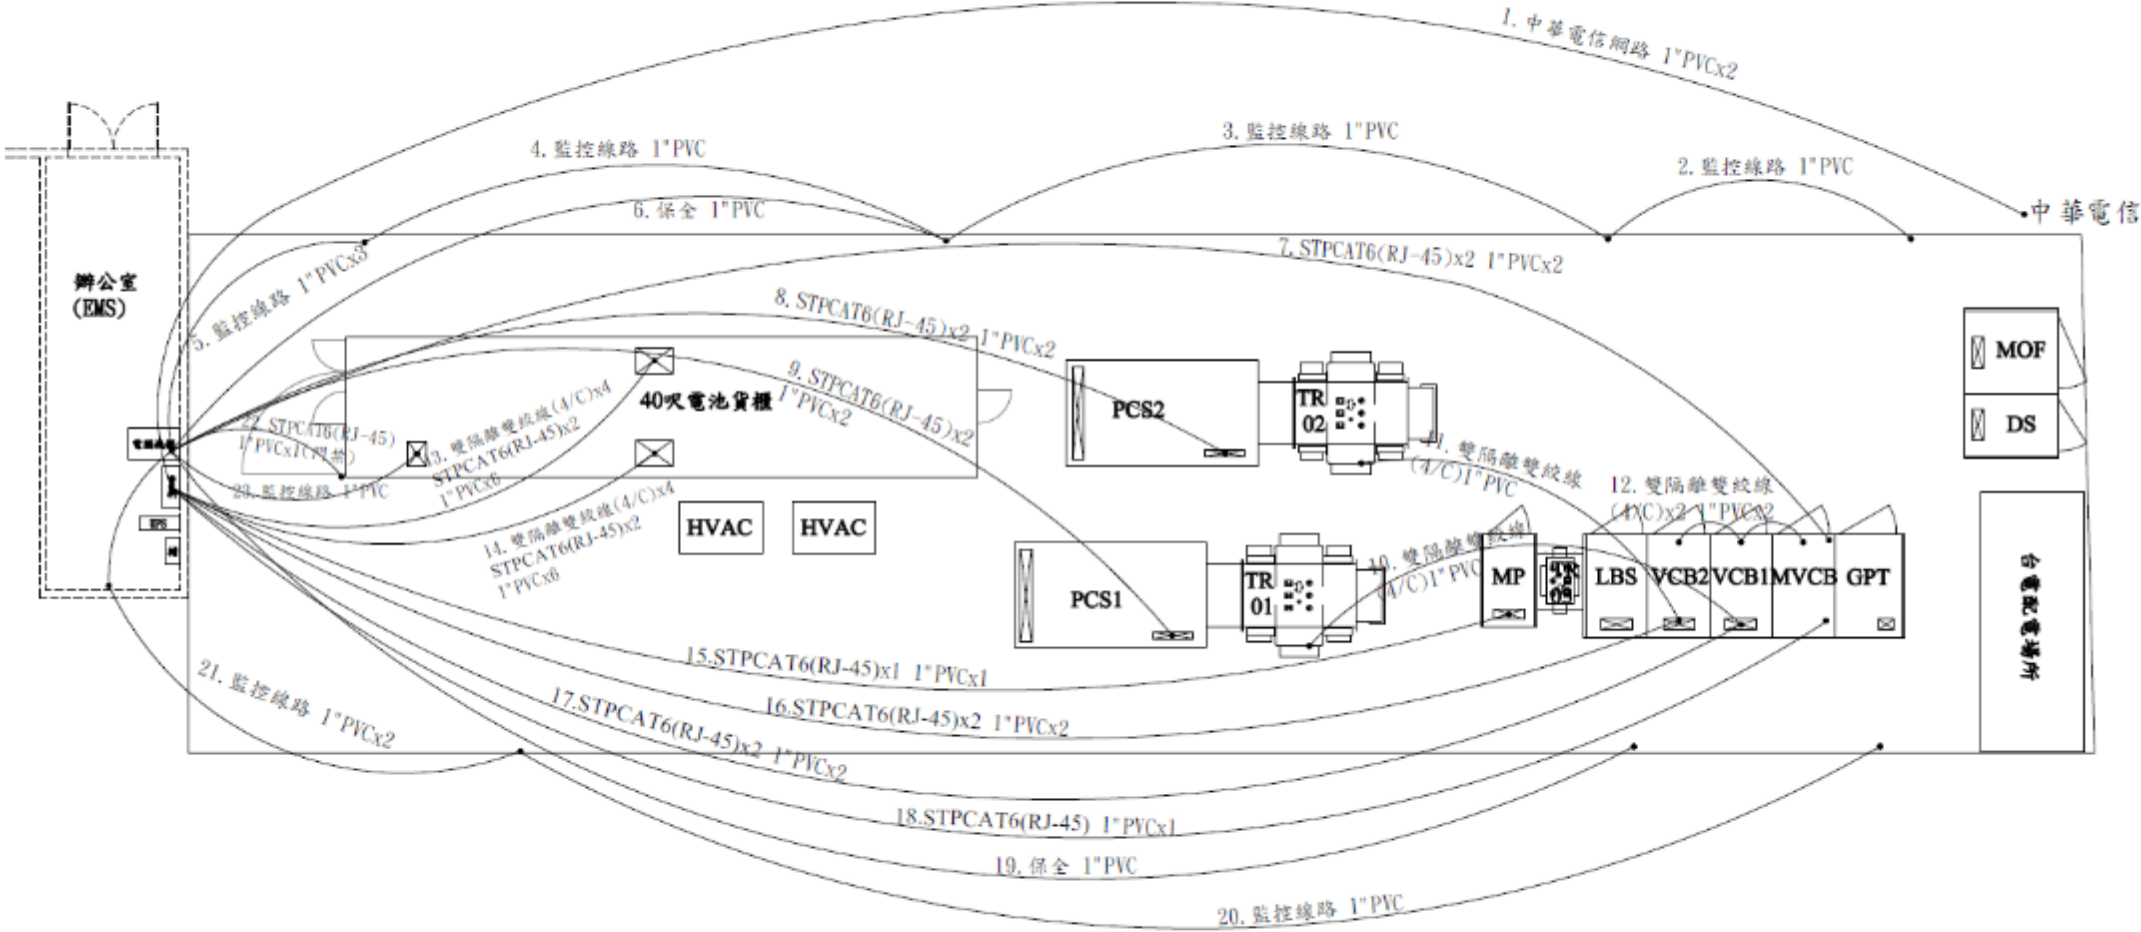


1
GL006 通訊及控制管線配置圖


配置圖

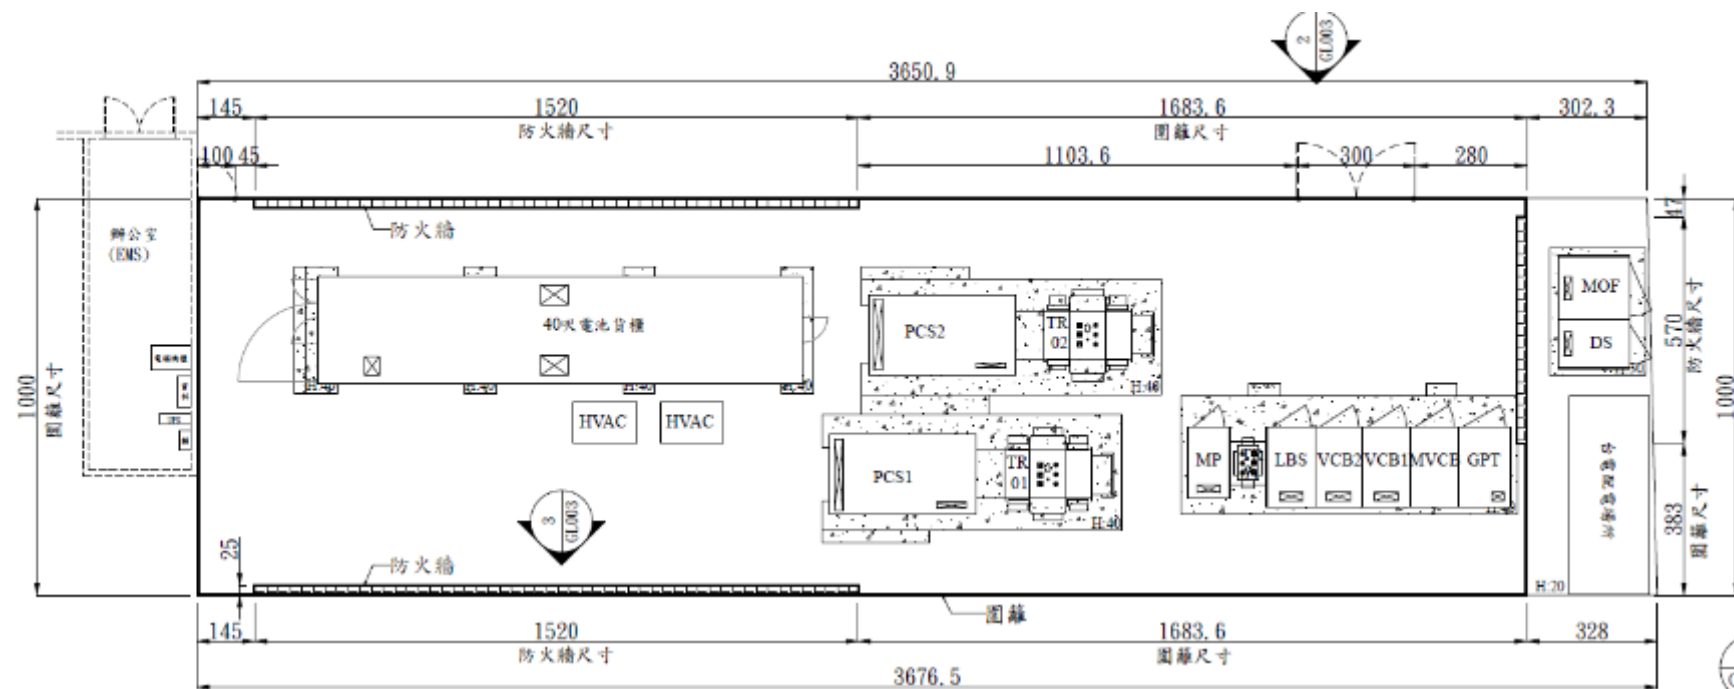

1 場域圍籬平面配置圖

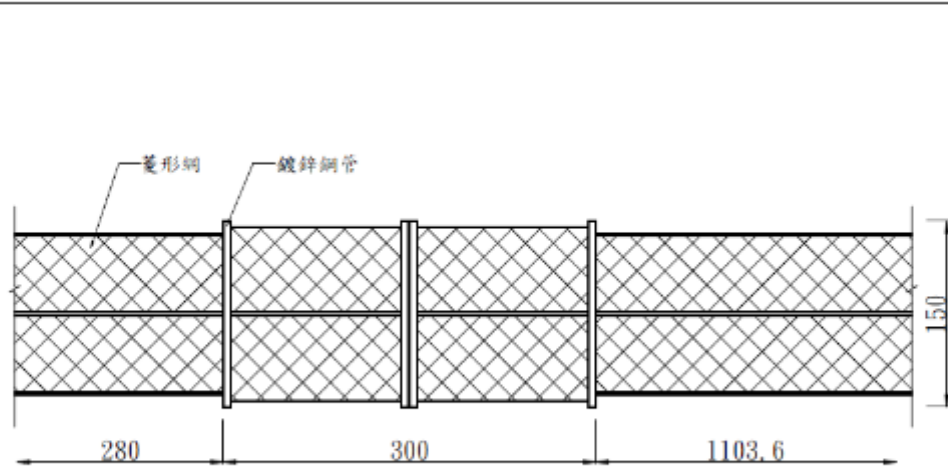


2 圍籬對開門立面圖

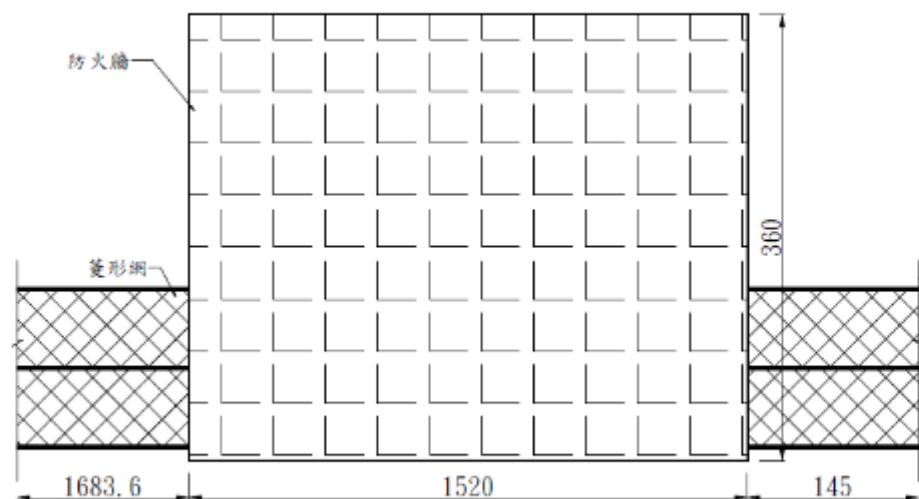

3 圍籬與防火牆示意圖

箱體圖

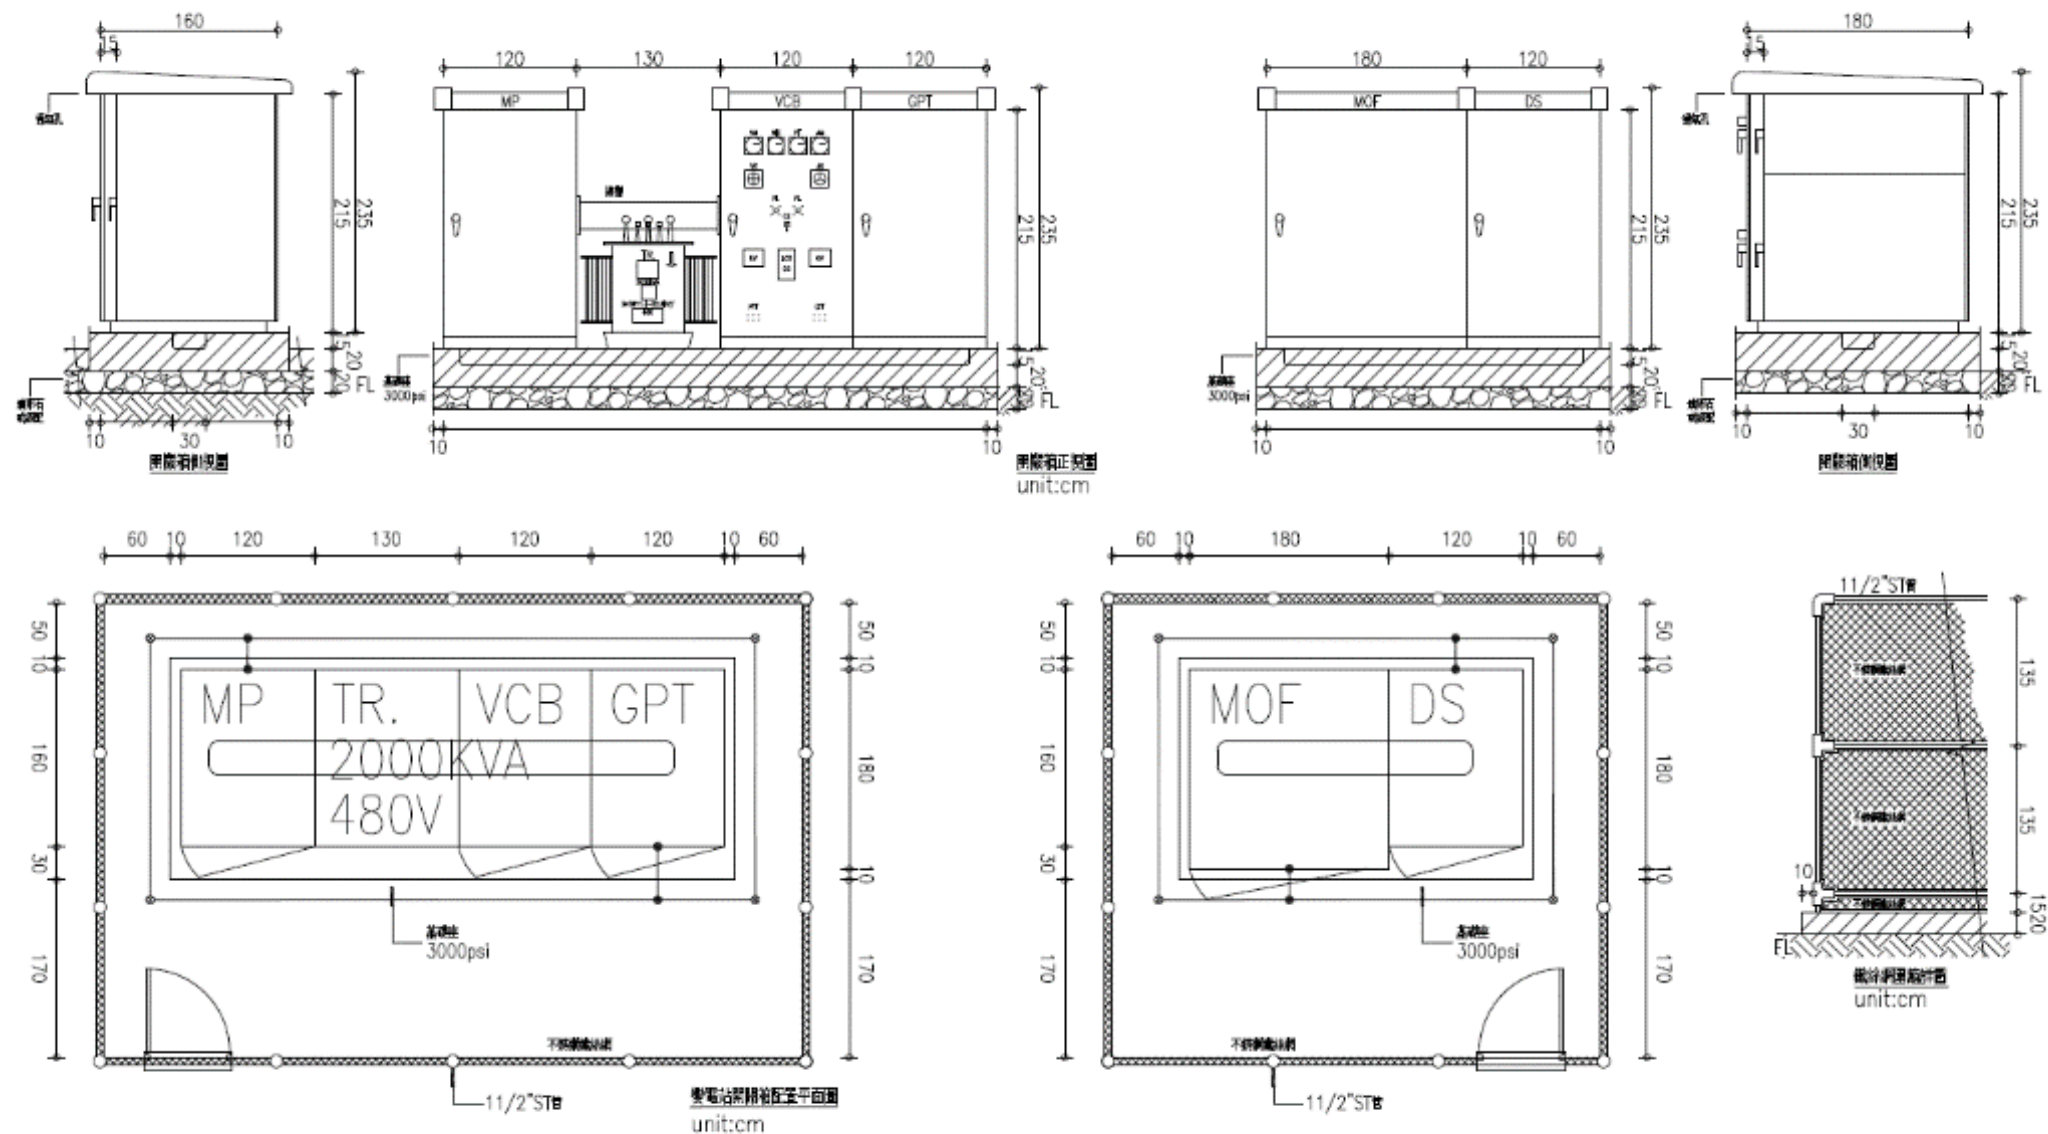

二、現場檢核



8M捲尺



50M捲尺




工程筆



螢光筆

圖面檢核工具

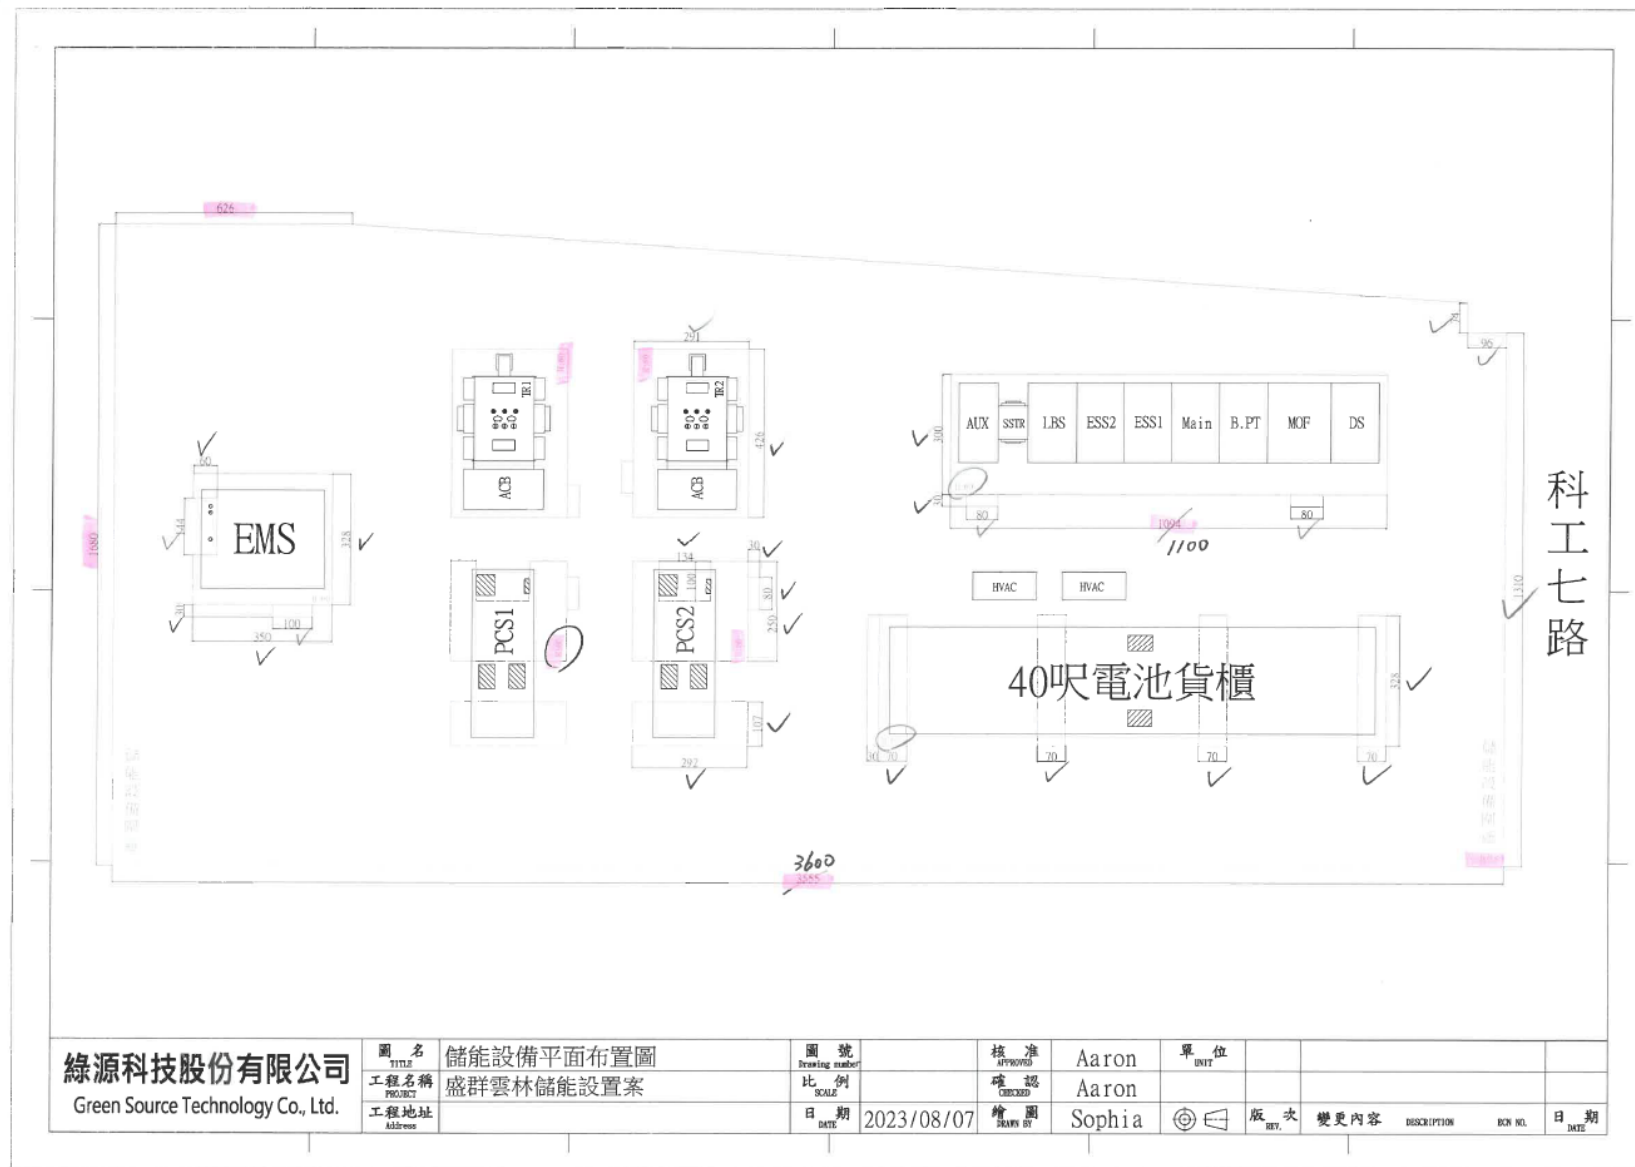

檢核標示

報告完畢！

